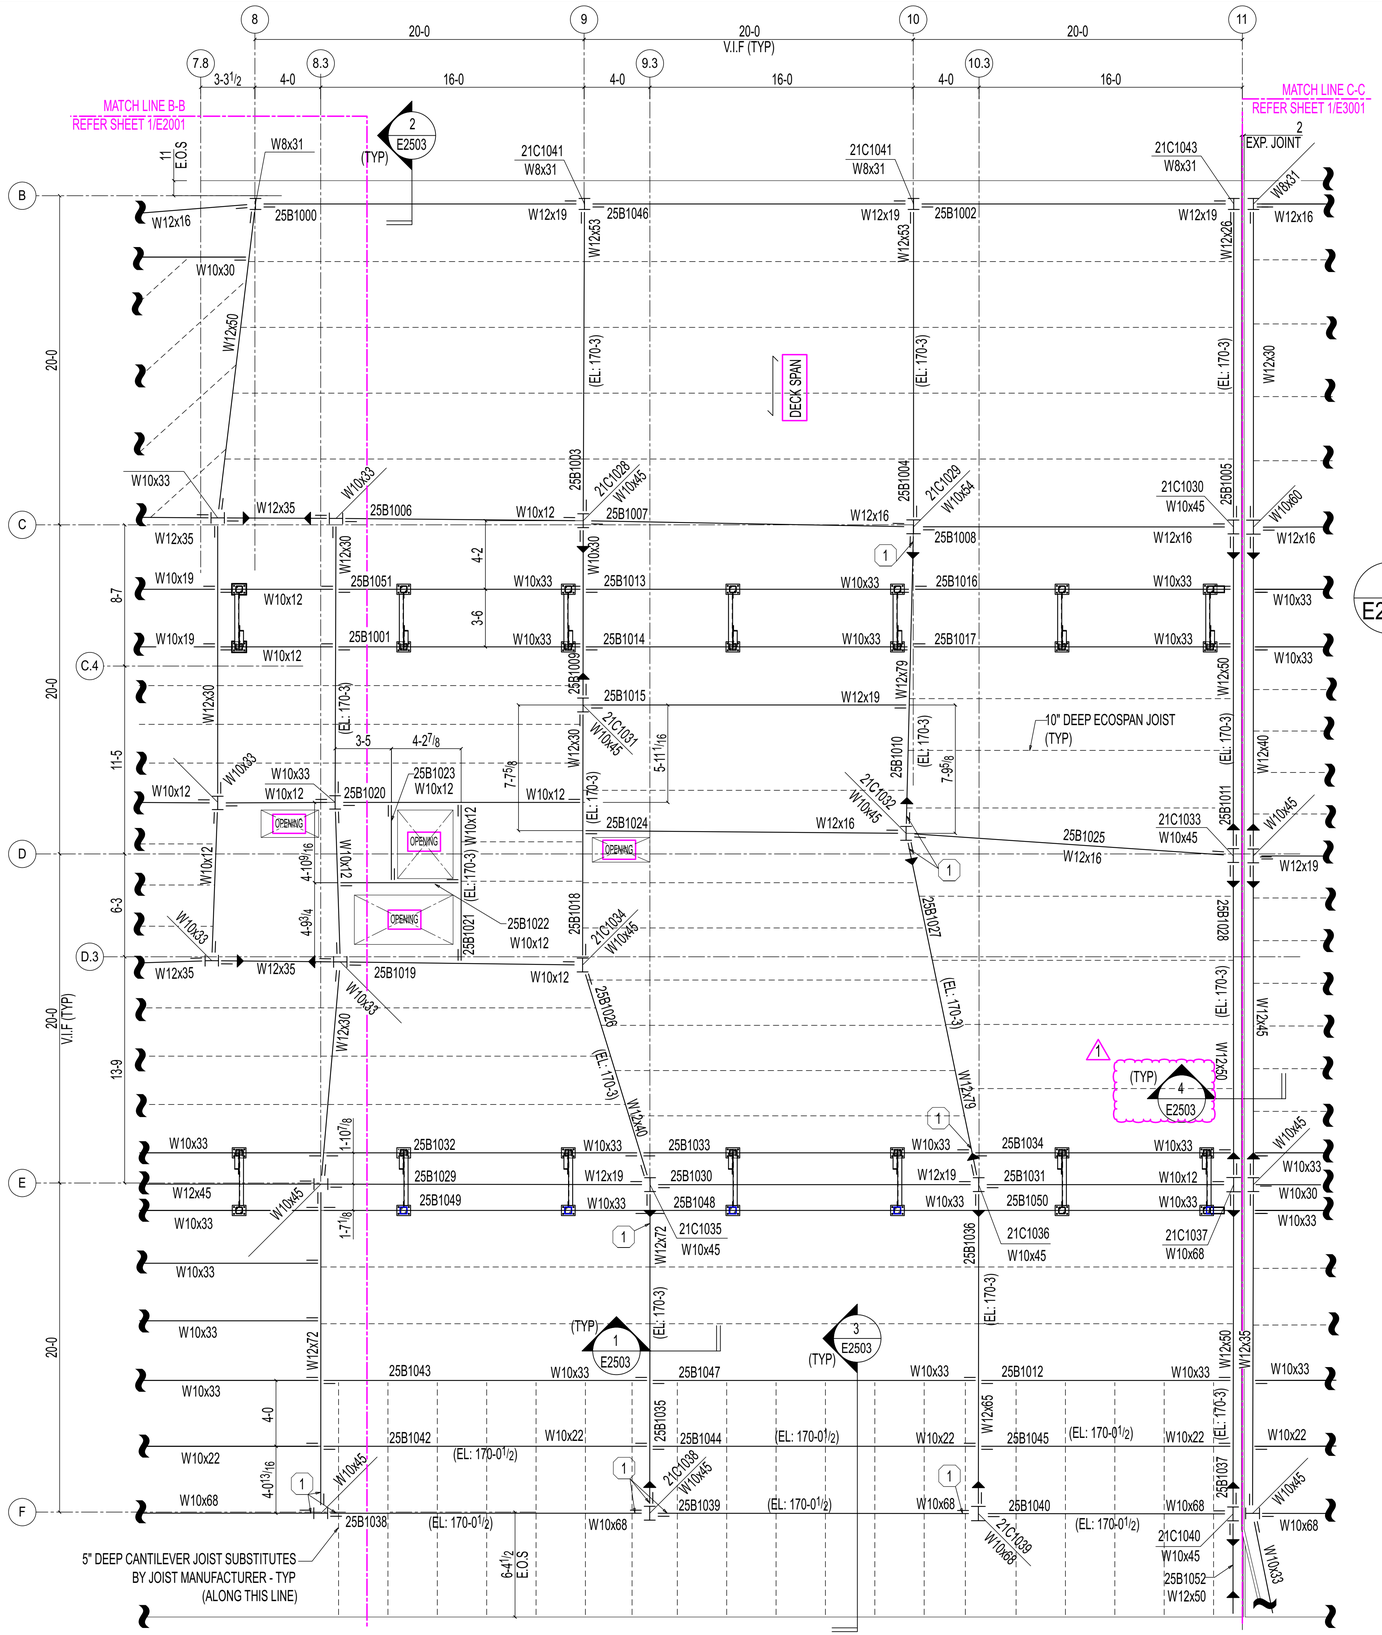

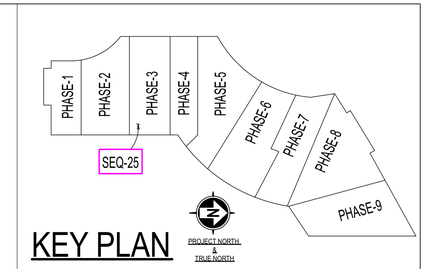

KEY PLAN

ERECTOR NOTES:
1.FOR CLARITY, ALL NEW STEEL COLUMN LOCATIONS & ROTATIONS ARE NOT SHOWN IN THIS PLAN. THEREFORE, PLEASE REFER TO SHEET 04AB01 FOR COLUMN LOCATIONS AND ROTATIONS (U.N.O).
2.ALL JOIST LOCATIONS ARE CO-ORDINATE WITH CORRESPONDING JOIST DRAWING.

1 / E2501 PARTIAL PENTHOUSE ROOF FRAMING PLAN (PHASE-3) (SEQ#25)

(REF: 1/S137_A & 1/S137_B)

NOTES:
1.TOP OF PENTHOUSE ROOF LEVEL SLAB EL: 170'-9" (U.N.O).
2.E.O.S - INDICATES EDGE OF SLAB.
3.▷ - DENOTES MOMENT CONNECTION.
4.ALL CONNECTION FIELD BOLTS SHALL BE 3/4" Ø F1852N TC BOLTS.(U.N.O).
5.ALL GRID DIMENSION TO BE VERIFY IN FIELD.(U.N.O).
6.⟷ - INDICATES METAL DECK SPAN ORIENTATION DIRECTION.
7.ELEVATION SHOWN ON PLAN ARE TO BE TOP OF BEAM (U.N.O)
8.ALL JOIST TO BE 10" DEEP ECOSPAN COMPOSITE FLOOR JOIST.(U.N.O).
9.TOP OF BEAM EL: 170'-5 1/2" (U.N.O).
10.ALL FIELD BOLTS SHALL BE SNUG TIGHTENED U.N.O.
11.(1)-DENOTES 1"Ø F2280N TC BOLTS FOR CONNECTION.
12.ALL BEAM LOCATING DIMENSIONS ARE PROVIDED FROM THE CENTER OF THE COLUMN, U.N.O.
13.– – – - INDICATES 10" DEEP ECOSPAN JOIST.(U.N.O)
14. REFER SHEET E2503 THRU E2506 FOR TYPICAL DETAILS.

PROJECT NORTH & TRUE NORTH

LEGEND:
TYP - TYPICAL
V.I.F - VERIFY IN FIELD
E.O.S - EDGE OF SLAB
U.N.O - UNLESS NOTED OTHERWISE
EL. - ELEVATION
T.O. - TOP OF

REVISIONS

REV#	DWN BY	DESCRIPTION	DATE
A	MNK	ISSUED FOR APPROVAL	Mar 15 2025
B	MNK	ISSUED FOR RE-APPROVAL	May 27 2025
0	MNK	ISSUED FOR CONSTRUCTION	Dec 12 2025
1	MNK	REVISED AS NOTED	Feb 4 2026

THE INFORMATION NOTED HEREON THIS DRAWING IS THE PROPERTY OF STEEL FAB ENTERPRISES, INC. AND SHALL NOTED BE USED WITHOUT WRITTEN CONSENT.

STEEL FAB ENTERPRISES, LLC
AISC CERTIFIED FABRICATOR AND ERECTOR
MISCELLANEOUS METALS FABRICATOR AND ERECTORS
623 BAUMGARDNER ROAD, LANCASTER, PA 17603
TEL. (717)464-0330 FAX (717)464-9464
WWW.STEELFABENTERPRISES.COM

PROJECT OWNER : HP NAREF, 1250 MARYLAND HOLDINGS 1 LP.
PROJECT DESCRIPTION : 1250 MARYLAND AVENUE
PROJECT ADDRESS : 1250 MARYLAND AVENUE, WASHINGTON, DC 20024
CONTRACTOR : IRON FABRICATION SERVICES, INC.

DRAWN BY : JSV	DATE : 02-27-2025	PROJ. NO. : 25001	REV # 1
CHECKED BY : MNK	DATE : 02-27-2025	DWG NO. : E2501	

DWG DESCRIPTION :PARTIAL PENTHOUSE ROOF FRAMING PLAN (PHASE-3) (SEQ#25)