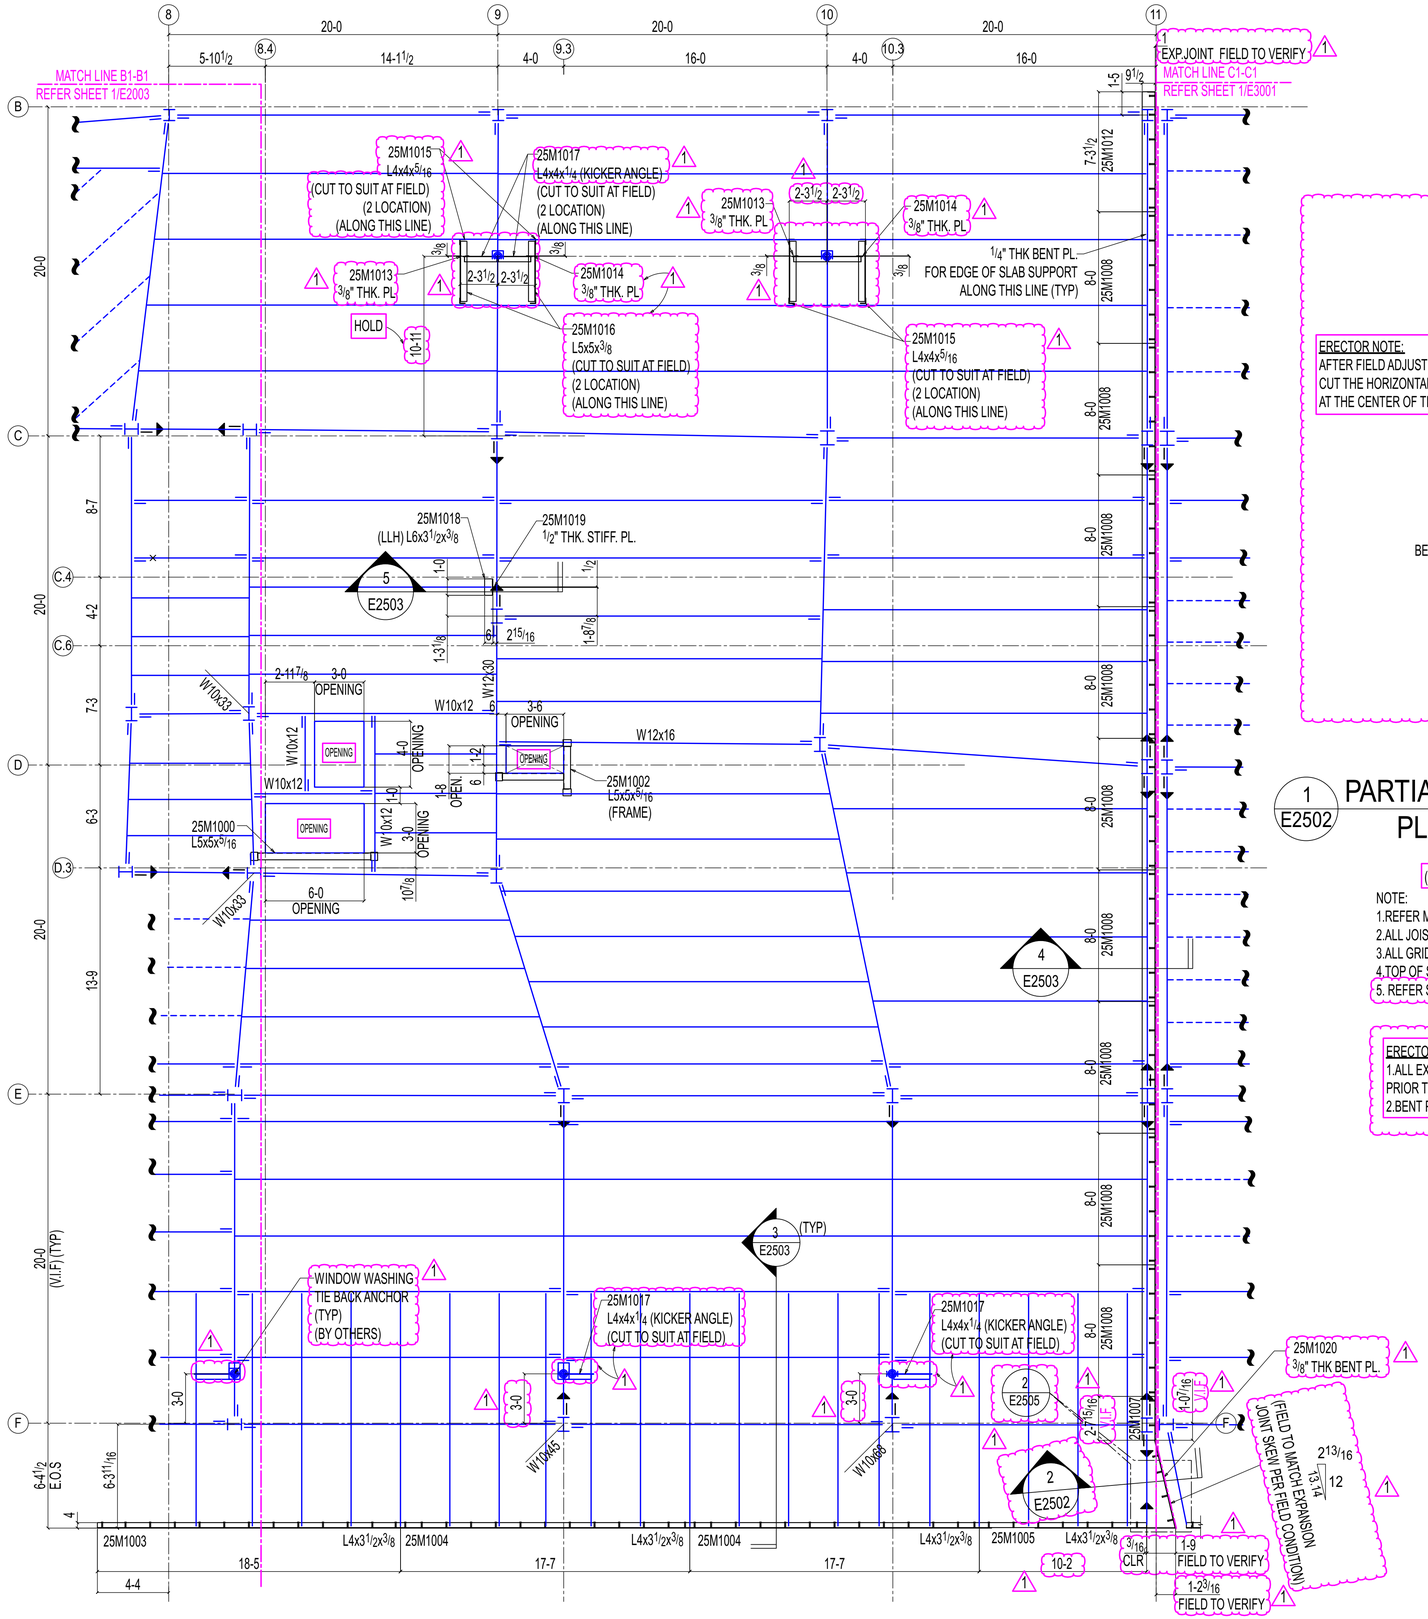

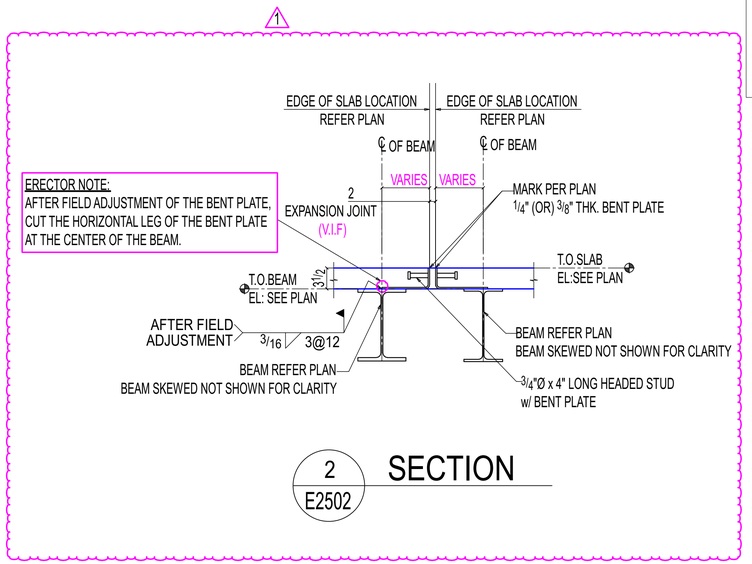

ERECTOR NOTE:
AFTER FIELD ADJUSTMENT OF THE BENT PLATE, CUT THE HORIZONTAL LEG OF THE BENT PLATE AT THE CENTER OF THE BEAM.

2 / E2502 SECTION

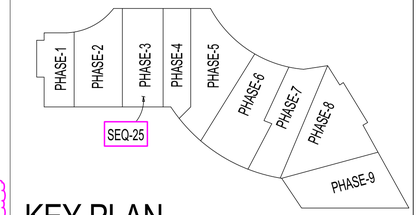

KEY PLAN

1 / E2502 PARTIAL PENTHOUSE ROOF MISC PLAN (PHASE-3) (SEQ#25)

(REF: 1/S137_A & 1/S137_B)

(OTHERS NOT SHOWN FOR CLARITY)

NOTE:
1. REFER MAIN FRAMING PLAN FOR ADDITIONAL INFORMATION
2. ALL JOIST TO BE 10" DEEP ECOSPAN COMPOSITE FLOOR JOIST.(U.N.O).
3. ALL GRID DIMENSION TO BE VERIFY IN FIELD.(U.N.O).
4. TOP OF SLAB EL:170'-9" (U.N.O).
5. REFER SHEET E2505 FOR TYPICAL TIEBACK ANCHOR SUPPORT DETAILS.

ERECTOR NOTE:
1. ALL EXPANSION JOINT LOCATIONS ARE TO BE VERIFIED IN THE FIELD, PRIOR TO INSTALL THE 1/4" THICK BENT PLATES.
2. BENT PLATES TO BE FIELD CUT AT CORNER PER FIELD CONDITION.

PROJECT NORTH
&
TRUE NORTH

REVISIONS

REV#	DWN BY	DESCRIPTION	DATE
A	MNK	ISSUED FOR APPROVAL	Mar 15 2025
B	MNK	ISSUED FOR RE-APPROVAL	May 27 2025
0	MNK	ISSUED FOR CONSTRUCTION	Dec 12 2025
1	MNK	REVISED AS NOTED	Feb 4 2026

THE INFORMATION NOTED HEREON THIS DRAWING IS THE PROPERTY OF STEEL FAB ENTERPRISES, INC. AND SHALL NOT BE USED WITHOUT WRITTEN CONSENT.

STEEL FAB
ENTERPRISES, LLC
AISC CERTIFIED FABRICATOR AND ERECTOR
MISCELLANEOUS METALS FABRICATOR AND ERECTORS
623 BAUMGARDNER ROAD, LANCASTER, PA 17603
TEL. (717)464-0330 FAX (717)464-9464
WWW.STEELFABENTERPRISES.COM

PROJECT OWNER : HP NAREF, 1250 MARYLAND HOLDINGS 1 LP.
PROJECT DESCRIPTION : 1250 MARYLAND AVENUE
PROJECT ADDRESS : 1250 MARYLAND AVENUE, WASHINGTON, DC 20024
CONTRACTOR : IRON FABRICATION SERVICES, INC.

DRAWN BY : JSV	DATE : 02-27-2025	PROJ. NO. :	25001	REV # 1
CHECKED BY : MNK	DATE : 02-27-2025	DWG NO. :	E2502	

DWG DESCRIPTION : PARTIAL PENTHOUSE ROOF MISC PLAN-(PHASE-3)(SEQ#25)